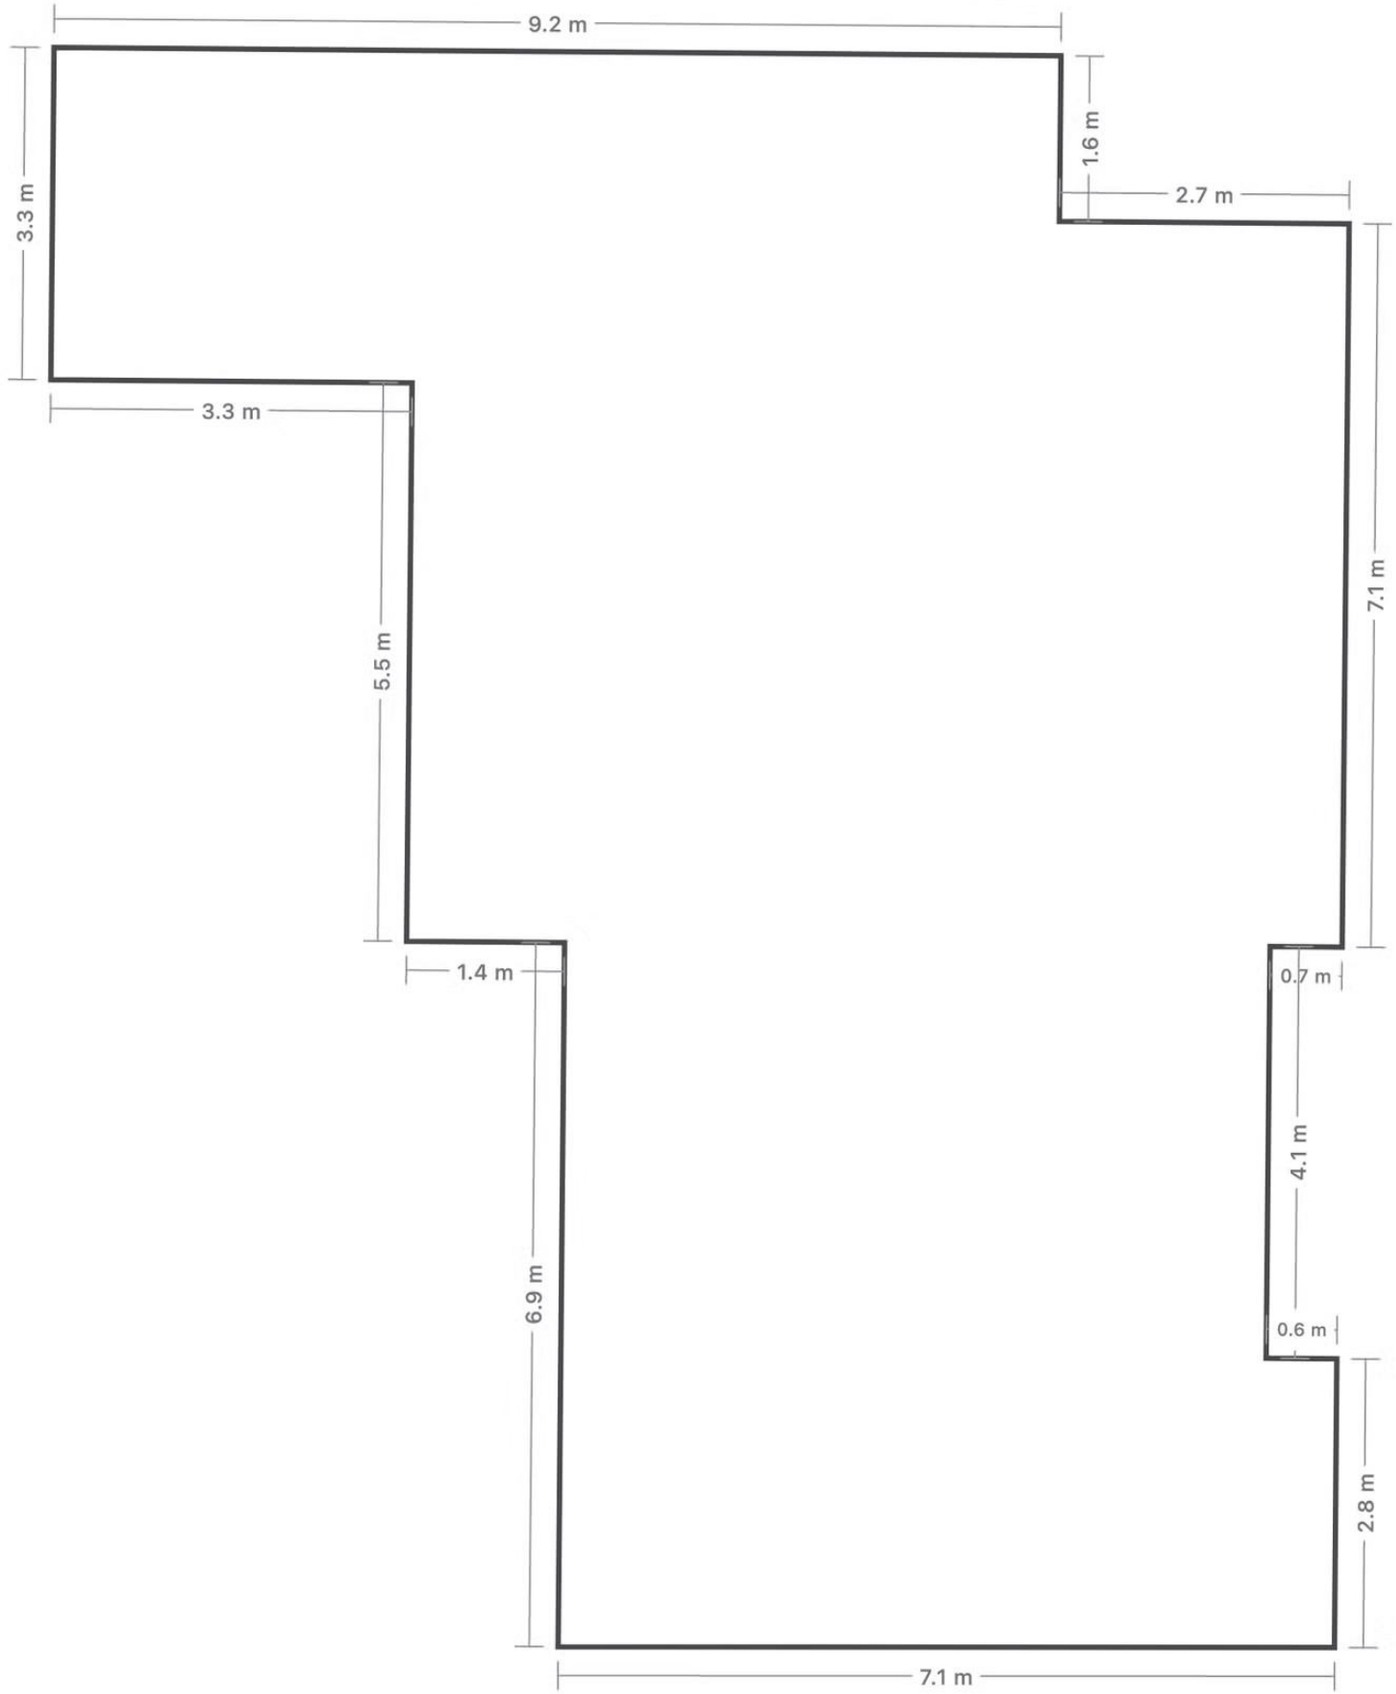
9.2 m
1.6 m
2.7 m
3.3 m
3.3 m
7.1 m
5.5 m
1.4 m
0.7 m
4.1 m
6.9 m
0.6 m
2.8 m
7.1 m

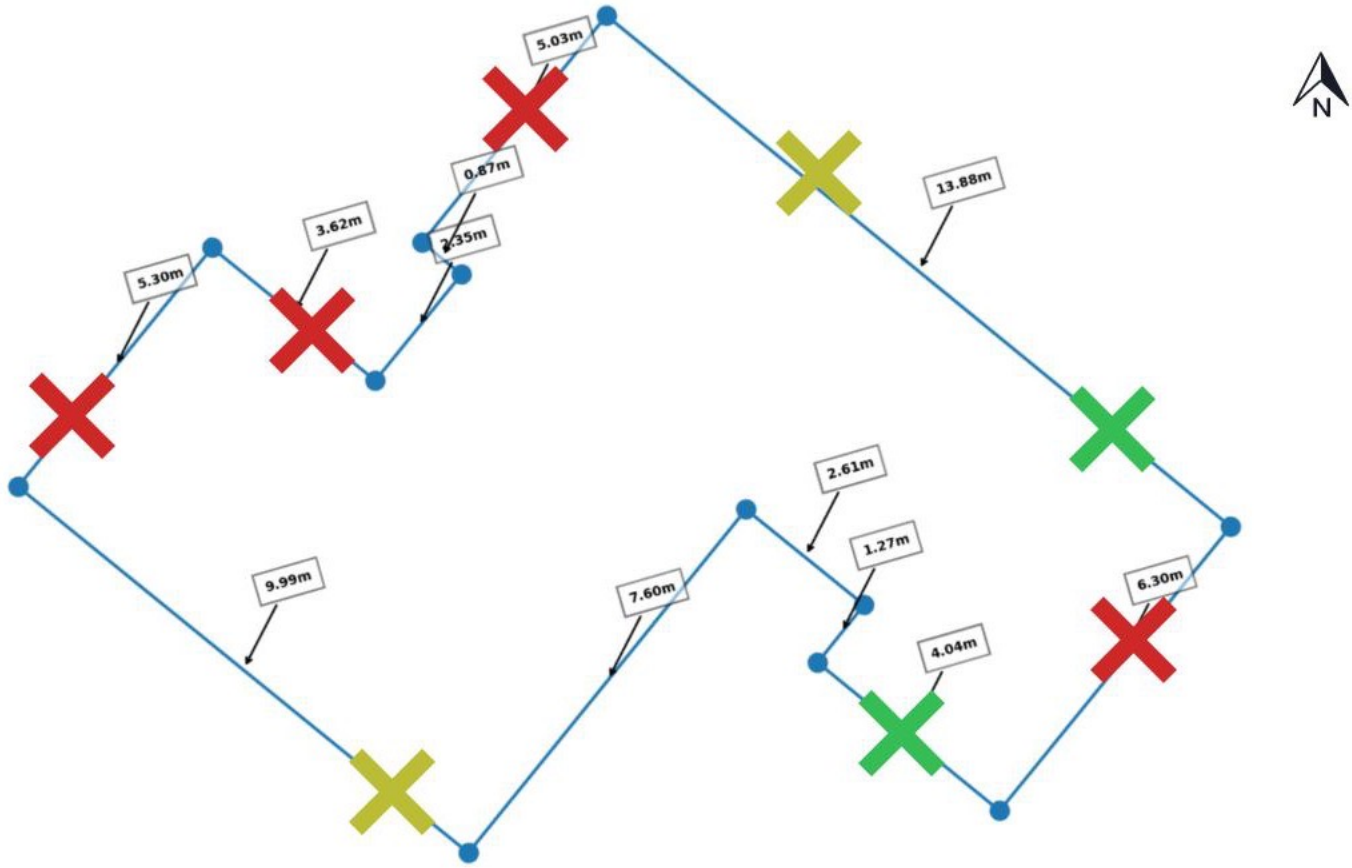

Erdgeschoss

Passt dieser Grundriss zum Erdgeschoss? ☑ Ja ☐ Nein ☐ Unsicher

Wenn '*nein*' oder '*unsicher*', bitte begründen:

	Typ des Fensterrahmens					Scheibenglas:		
Fenstertypen	Kunstoff	Holz	Alu	Stahl	Holz & Alu	1	2	3
Fenstertyp 1 Jahr : 1972	☐	☑	☐	☐	☐	☐	☑	☐
Fenstertyp 2 Jahr: 1992	☑	☐	☐	☐	☐	☑	☐	☐
Fenstertyp 3 Jahr: 2020	☑	☐	☐	☐	☐	☐	☑	☐
Fenstertyp 4 Jahr:	☐	☐	☐	☐	☐	☐	☐	☐